


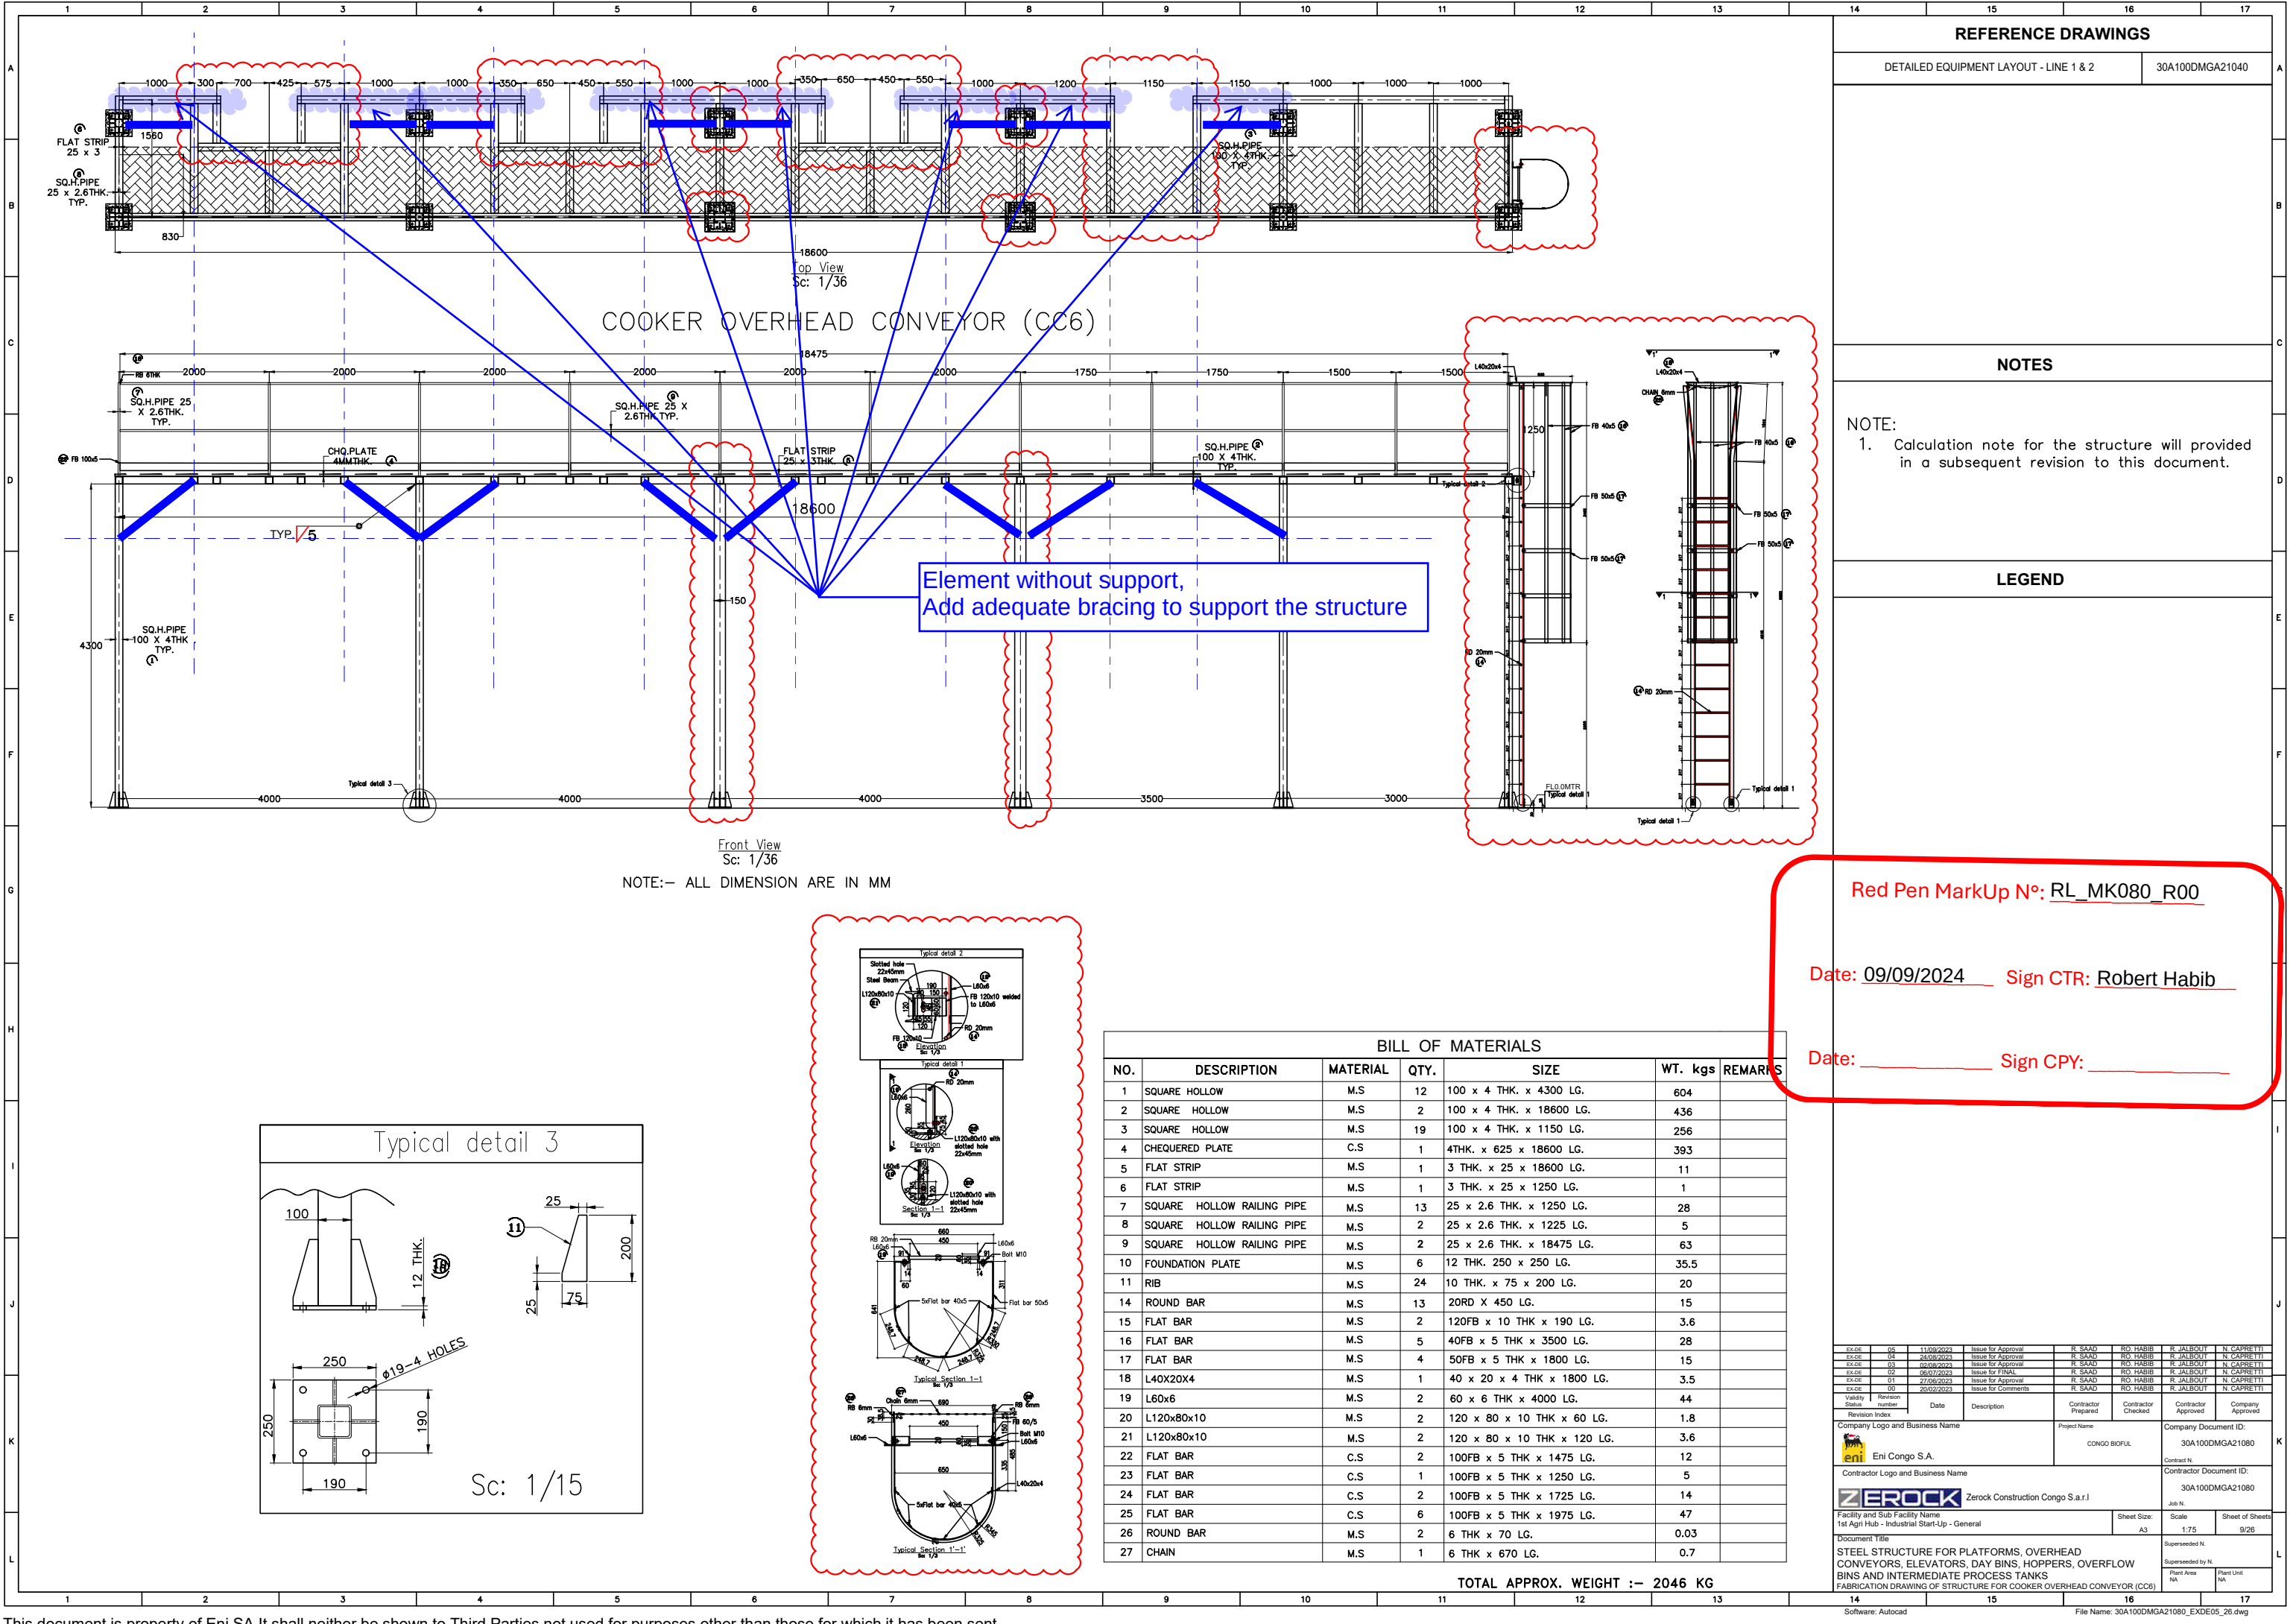

Red Pen Markup N°: RL_MK080_R00

Date: 09/09/2024 Sign CTR: Robert Habib

Date: _____ Sign CPY: _____

BILL OF MATERIALS

NO.	DESCRIPTION	MATERIAL	QTY.	SIZE	WT. kgs	REMARKS
1	SQUARE HOLLOW	M.S	12	100 x 4 THK. x 4300 LG.	604	
2	SQUARE HOLLOW	M.S	2	100 x 4 THK. x 18600 LG.	436	
3	SQUARE HOLLOW	M.S	19	100 x 4 THK. x 1150 LG.	256	
4	CHEQUERED PLATE	C.S	1	4THK. x 625 x 18600 LG.	393	
5	FLAT STRIP	M.S	1	3 THK. x 25 x 18600 LG.	11	
6	FLAT STRIP	M.S	1	3 THK. x 25 x 1250 LG.	1	
7	SQUARE HOLLOW RAILING PIPE	M.S	13	25 x 2.6 THK. x 1250 LG.	28	
8	SQUARE HOLLOW RAILING PIPE	M.S	2	25 x 2.6 THK. x 1225 LG.	5	
9	SQUARE HOLLOW RAILING PIPE	M.S	2	25 x 2.6 THK. x 18475 LG.	63	
10	FOUNDATION PLATE	M.S	6	12 THK. 250 x 250 LG.	35.5	
11	RIB	M.S	24	10 THK. x 75 x 200 LG.	20	
14	ROUND BAR	M.S	13	20RD X 450 LG.	15	
15	FLAT BAR	M.S	2	120FB x 10 THK x 190 LG.	3.6	
16	FLAT BAR	M.S	5	40FB x 5 THK x 3500 LG.	28	
17	FLAT BAR	M.S	4	50FB x 5 THK x 1800 LG.	15	
18	L40X20X4	M.S	1	40 x 20 x 4 THK x 1800 LG.	3.5	
19	L60x6	M.S	2	60 x 6 THK x 4000 LG.	44	
20	L120x80x10	M.S	2	120 x 80 x 10 THK x 60 LG.	1.8	
21	L120x80x10	M.S	2	120 x 80 x 10 THK x 120 LG.	3.6	
22	FLAT BAR	C.S	2	100FB x 5 THK x 1475 LG.	12	
23	FLAT BAR	C.S	1	100FB x 5 THK x 1250 LG.	5	
24	FLAT BAR	C.S	2	100FB x 5 THK x 1725 LG.	14	
25	FLAT BAR	C.S	6	100FB x 5 THK x 1975 LG.	47	
26	ROUND BAR	M.S	2	6 THK x 70 LG.	0.03	
27	CHAIN	M.S	1	6 THK x 670 LG.	0.7	

TOTAL APPROX. WEIGHT :- 2046 KG

REFERENCE DRAWINGS

DETAILED EQUIPMENT LAYOUT - LINE 1 & 2 30A100DMGA21040

NOTES

NOTE:
1. Calculation note for the structure will provided in a subsequent revision to this document.

LEGEND

EX-05	05	11/09/2023	Issue for Approval	R. SAAD	RO. HABIB	R. JALBOUT	N. CAPRETTI
EX-05	04	23/08/2023	Issue for Approval	R. SAAD	RO. HABIB	R. JALBOUT	N. CAPRETTI
EX-05	03	09/08/2023	Issue for Approval	R. SAAD	RO. HABIB	R. JALBOUT	N. CAPRETTI
EX-05	02	06/07/2023	Issue for FINAL	R. SAAD	RO. HABIB	R. JALBOUT	N. CAPRETTI
EX-05	01	27/06/2023	Issue for Approval	R. SAAD	RO. HABIB	R. JALBOUT	N. CAPRETTI
EX-05	00	20/02/2023	Issue for Comments	R. SAAD	RO. HABIB	R. JALBOUT	N. CAPRETTI
Validity	Revision	Date	Description	Contractor Prepared	Contractor Checked	Contractor Approved	Company Approved
Revision Index	Revision number						
Company Logo and Business Name				Project Name		Company Document ID:	
Eni Congo S.A.				CONGO BIOFUL		30A100DMGA21080	
Contractor Logo and Business Name				Contract N°		Contractor Document ID:	
ZEROCK				Zerock Construction Congo S.a.r.l		30A100DMGA21080	
Facility and Sub Facility Name				Sheet Size:		Sheet of Sheets:	
1st Agri Hub - Industrial Start-Up - General				A3		1/75 9/26	
Document Title				Superseded N°		Superseded by N°	
STEEL STRUCTURE FOR PLATFORMS, OVERHEAD CONVEYORS, ELEVATORS, DAY BINS, HOPPERS, OVERFLOW BINS AND INTERMEDIATE PROCESS TANKS				Plant Area		Plant Unit	
FABRICATION DRAWING OF STRUCTURE FOR COOKER OVERHEAD CONVEYOR (CC6)				NA		NA	