







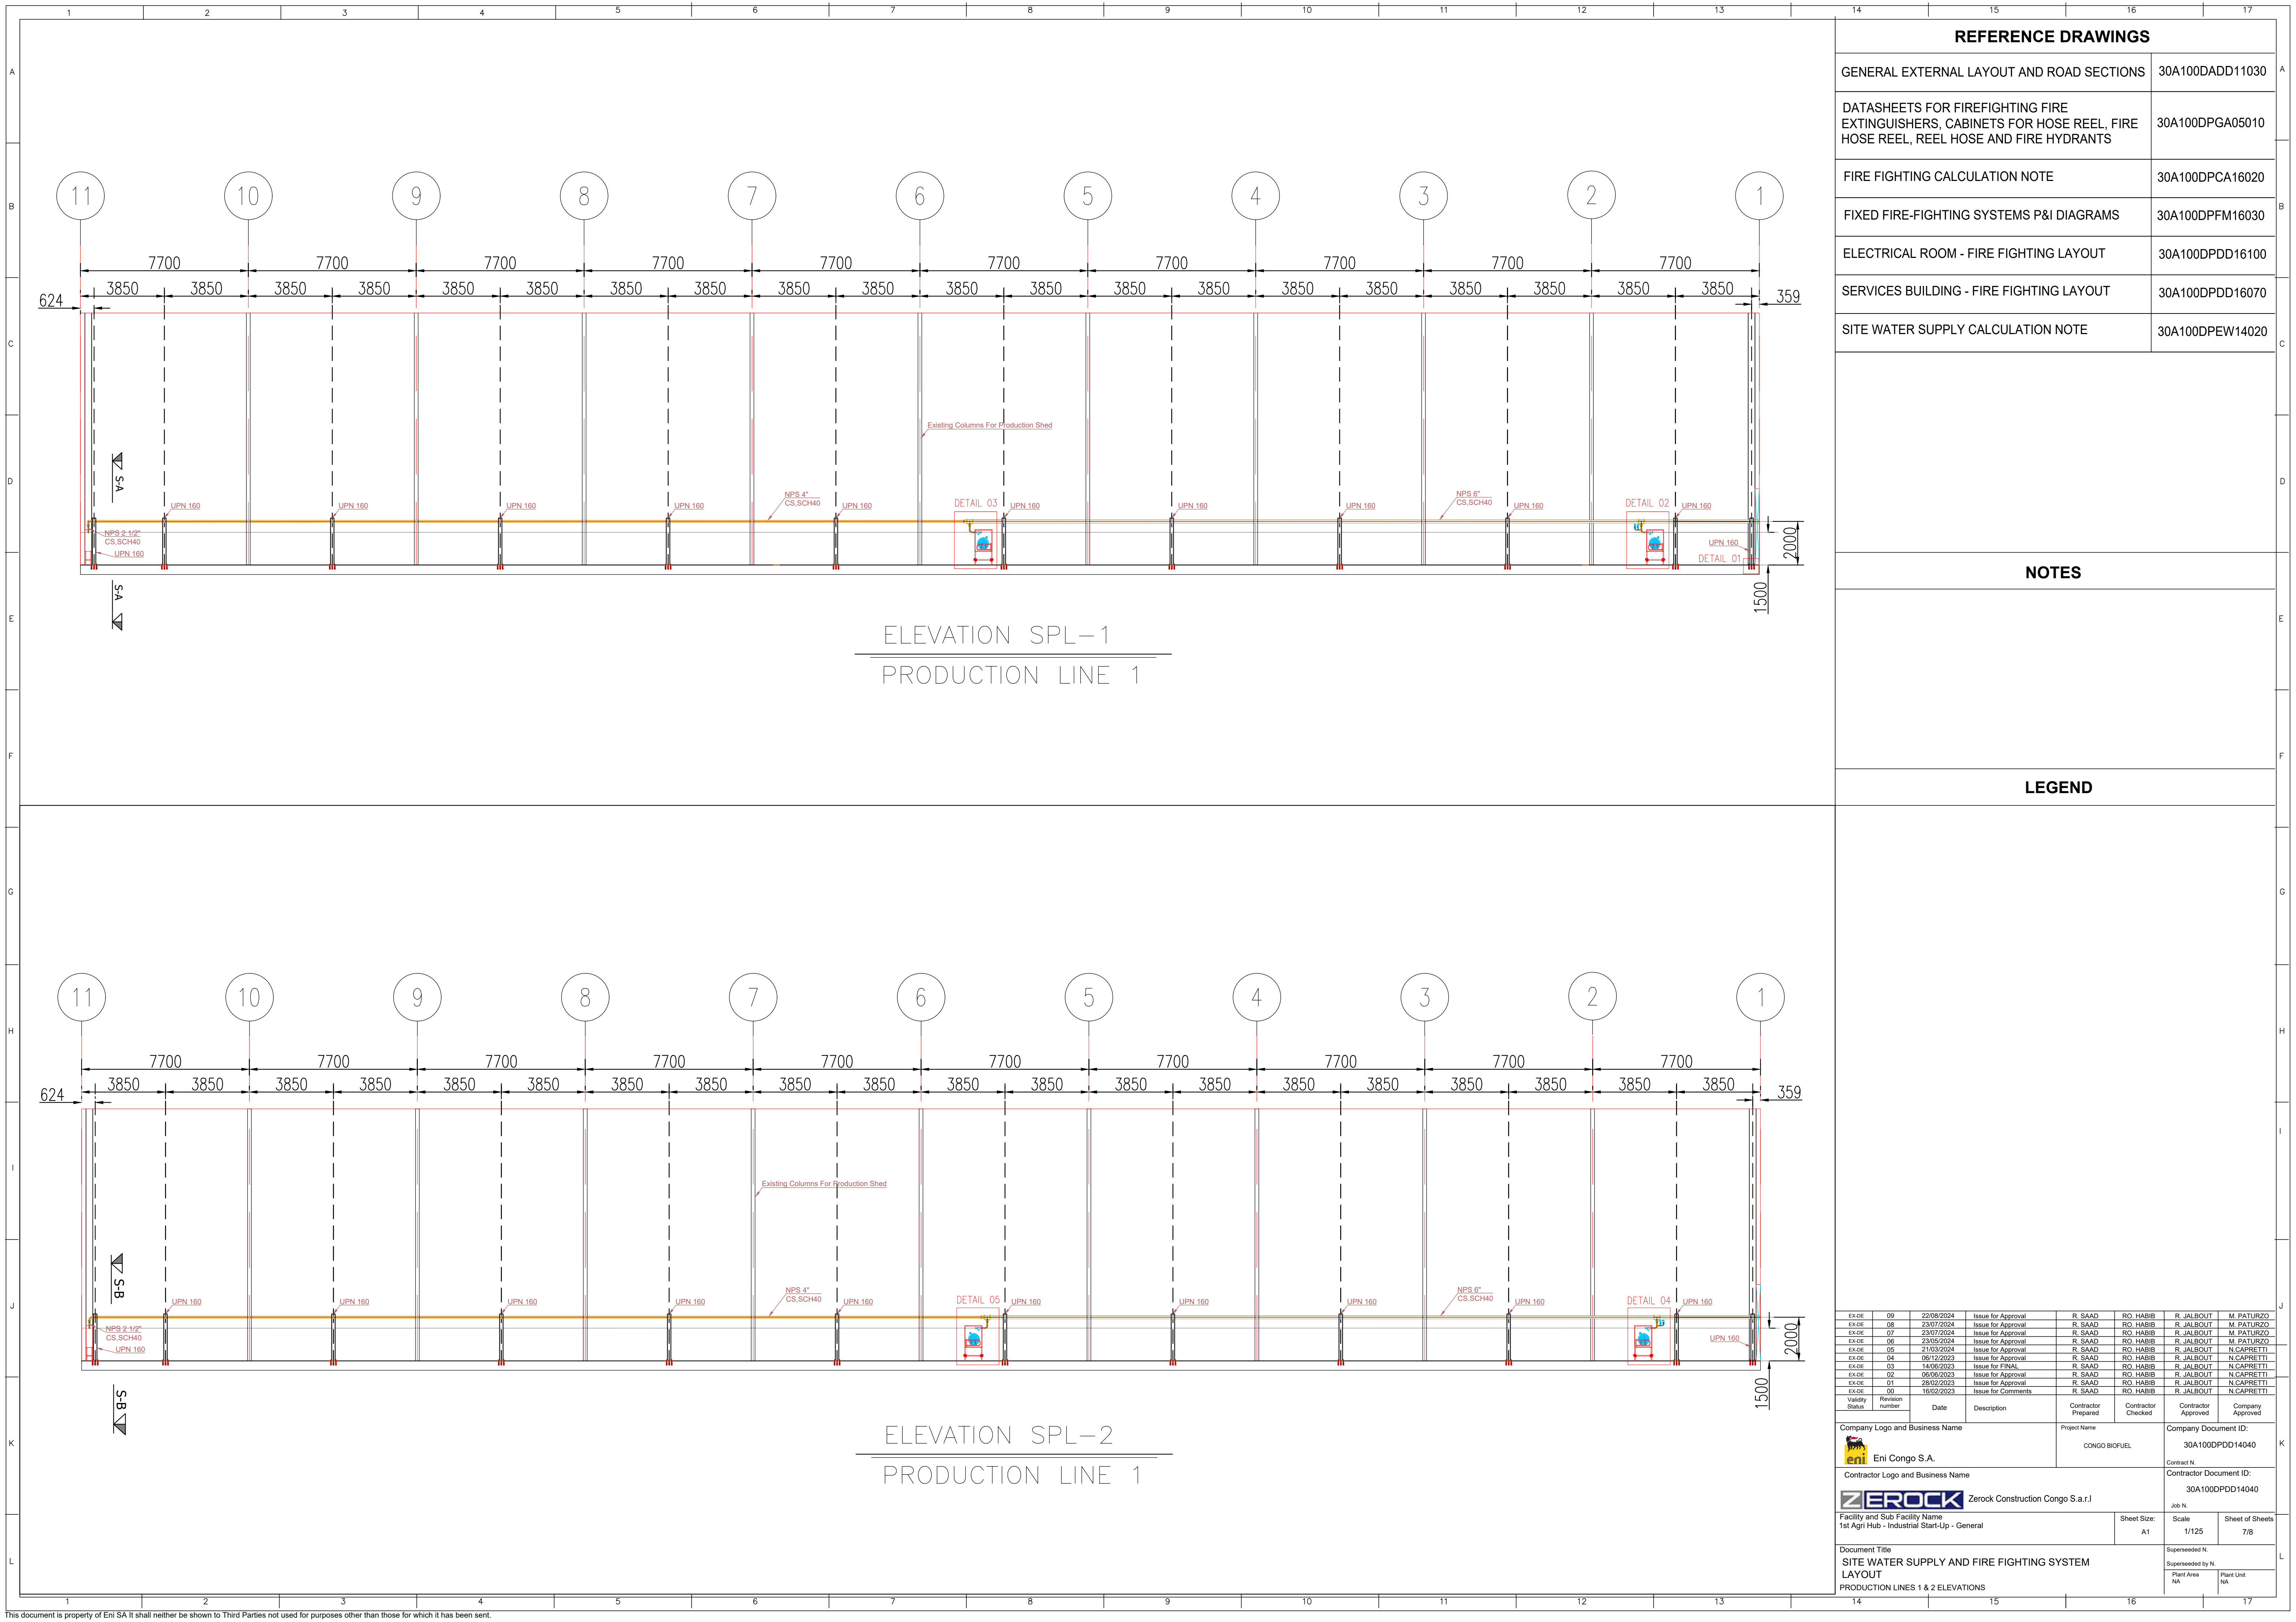


REFERENCE DRAWINGS	
GENERAL EXTERNAL LAYOUT AND ROAD SECTIONS	30A100DADD11030
DATASHEETS FOR FIREFIGHTING FIRE EXTINGUISHERS, CABINETS FOR HOSE REEL, FIRE HOSE REEL, REEL HOSE AND FIRE HYDRANTS	30A100DPGA05010
FIRE FIGHTING CALCULATION NOTE	30A100DPCA16020
FIXED FIRE-FIGHTING SYSTEMS P&I DIAGRAMS	30A100DPFM16030
ELECTRICAL ROOM - FIRE FIGHTING LAYOUT	30A100DPDD16100
SERVICES BUILDING - FIRE FIGHTING LAYOUT	30A100DPDD16070
SITE WATER SUPPLY CALCULATION NOTE	30A100DPEW14020



NOTES	

LEGEND	

EX-DE	09	22/08/2024	Issue for Approval	R. SAAD	RO. HABIB	R. JALBOUT	M. PATURZO
EX-DE	08	23/07/2024	Issue for Approval	R. SAAD	RO. HABIB	R. JALBOUT	M. PATURZO
EX-DE	07	23/07/2024	Issue for Approval	R. SAAD	RO. HABIB	R. JALBOUT	M. PATURZO
EX-DE	06	23/05/2024	Issue for Approval	R. SAAD	RO. HABIB	R. JALBOUT	M. PATURZO
EX-DE	05	21/03/2024	Issue for Approval	R. SAAD	RO. HABIB	R. JALBOUT	N. CAPRETTI
EX-DE	04	06/12/2023	Issue for Approval	R. SAAD	RO. HABIB	R. JALBOUT	N. CAPRETTI
EX-DE	03	14/06/2023	Issue for FINAL	R. SAAD	RO. HABIB	R. JALBOUT	N. CAPRETTI
EX-DE	02	06/06/2023	Issue for Approval	R. SAAD	RO. HABIB	R. JALBOUT	N. CAPRETTI
EX-DE	01	28/02/2023	Issue for Approval	R. SAAD	RO. HABIB	R. JALBOUT	N. CAPRETTI
EX-DE	00	16/02/2023	Issue for Comments	R. SAAD	RO. HABIB	R. JALBOUT	N. CAPRETTI
Validity Status	Revision number	Date	Description	Contractor Prepared	Contractor Checked	Contractor Approved	Company Approved
Company Logo and Business Name				Project Name		Company Document ID:	
Eni Congo S.A.				CONGO BIOFUEL		30A100PDD14040	
Contractor Logo and Business Name				Contract N.		Contractor Document ID:	
Zero Rock Construction Congo S.a.r.l				Job N.		30A100PDD14040	
Facility and Sub Facility Name				Sheet Size:	Scale	Sheet of Sheets	
1st Agri Hub - Industrial Start-Up - General				A1	1/125	7/8	
Document Title						Superseded by N.	
SITE WATER SUPPLY AND FIRE FIGHTING SYSTEM LAYOUT						Plant Area NA	Plant Unit NA
PRODUCTION LINES 1 & 2 ELEVATIONS							

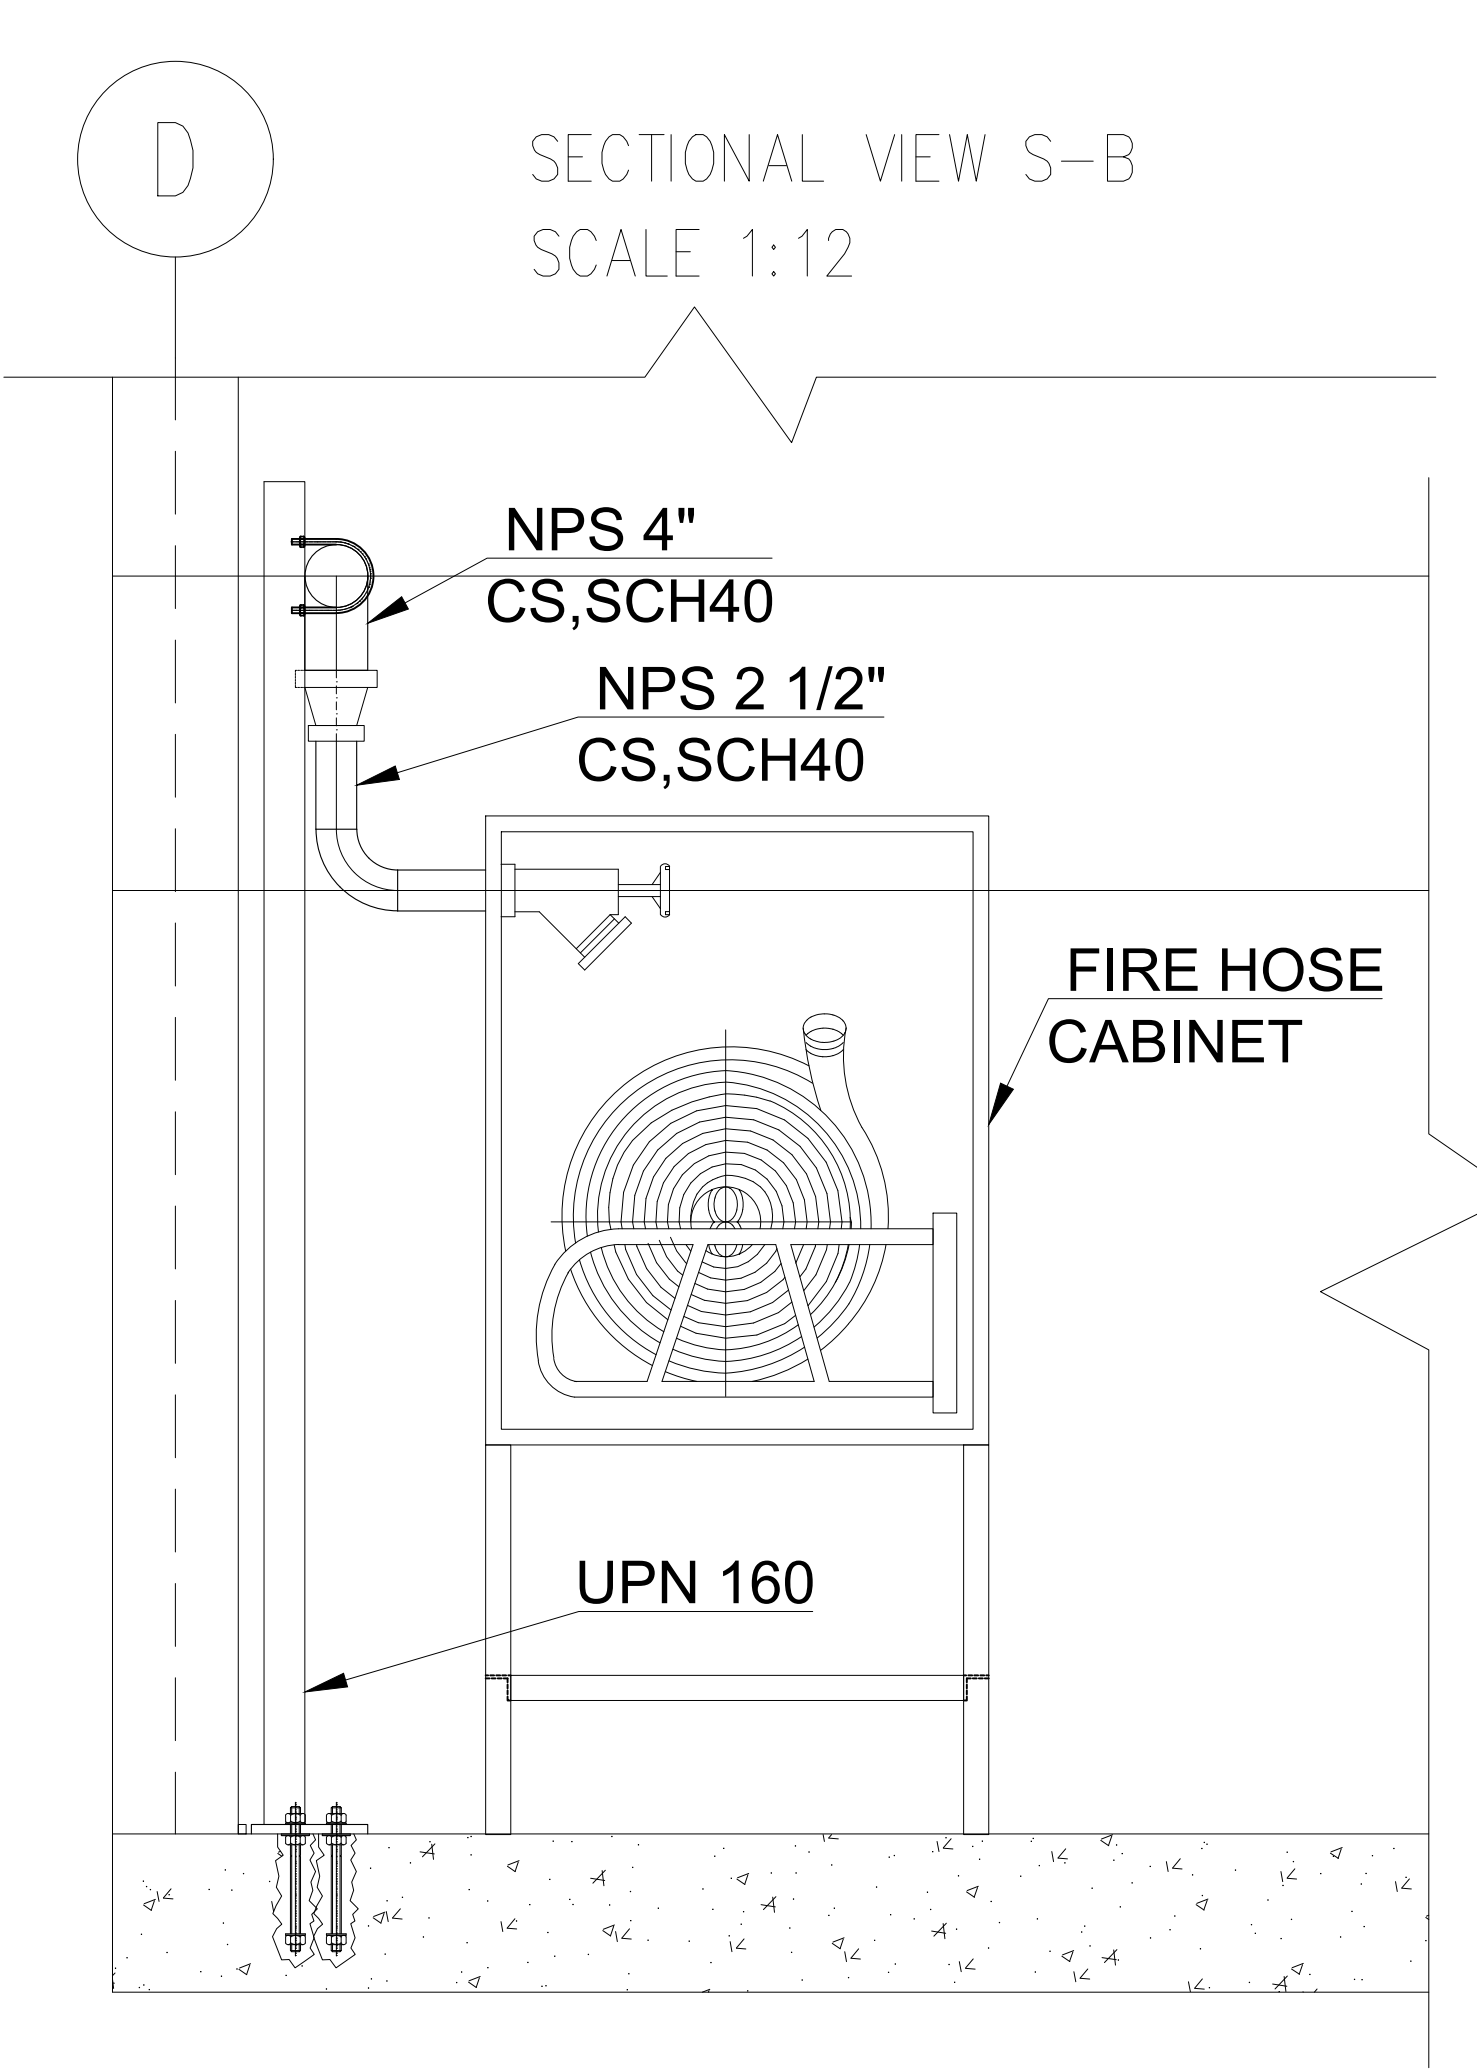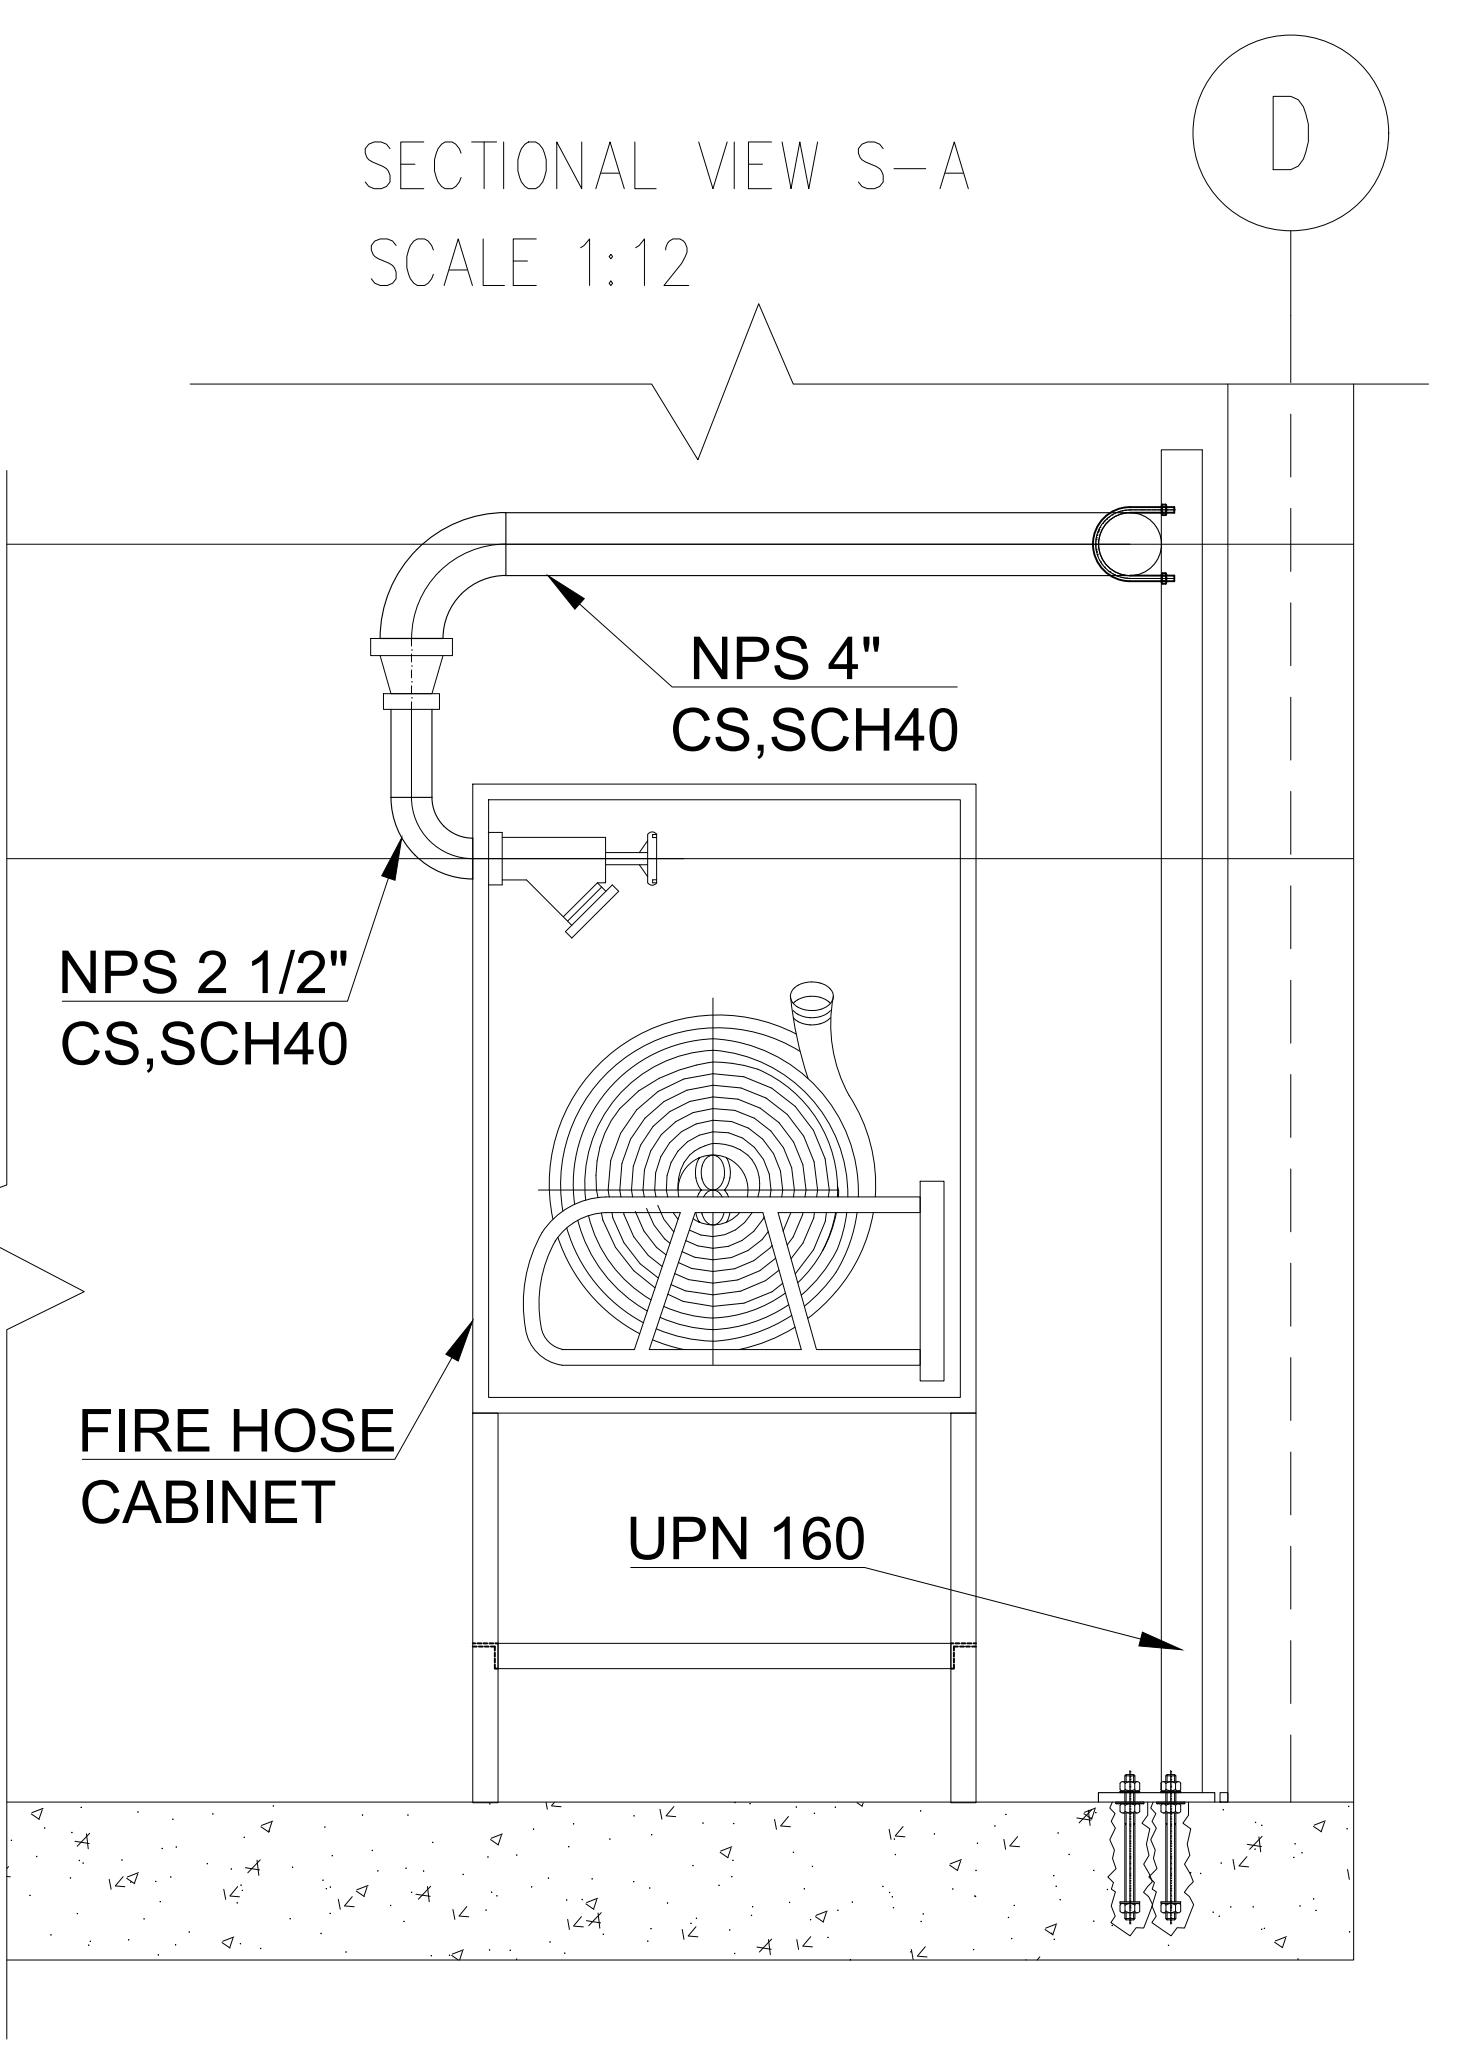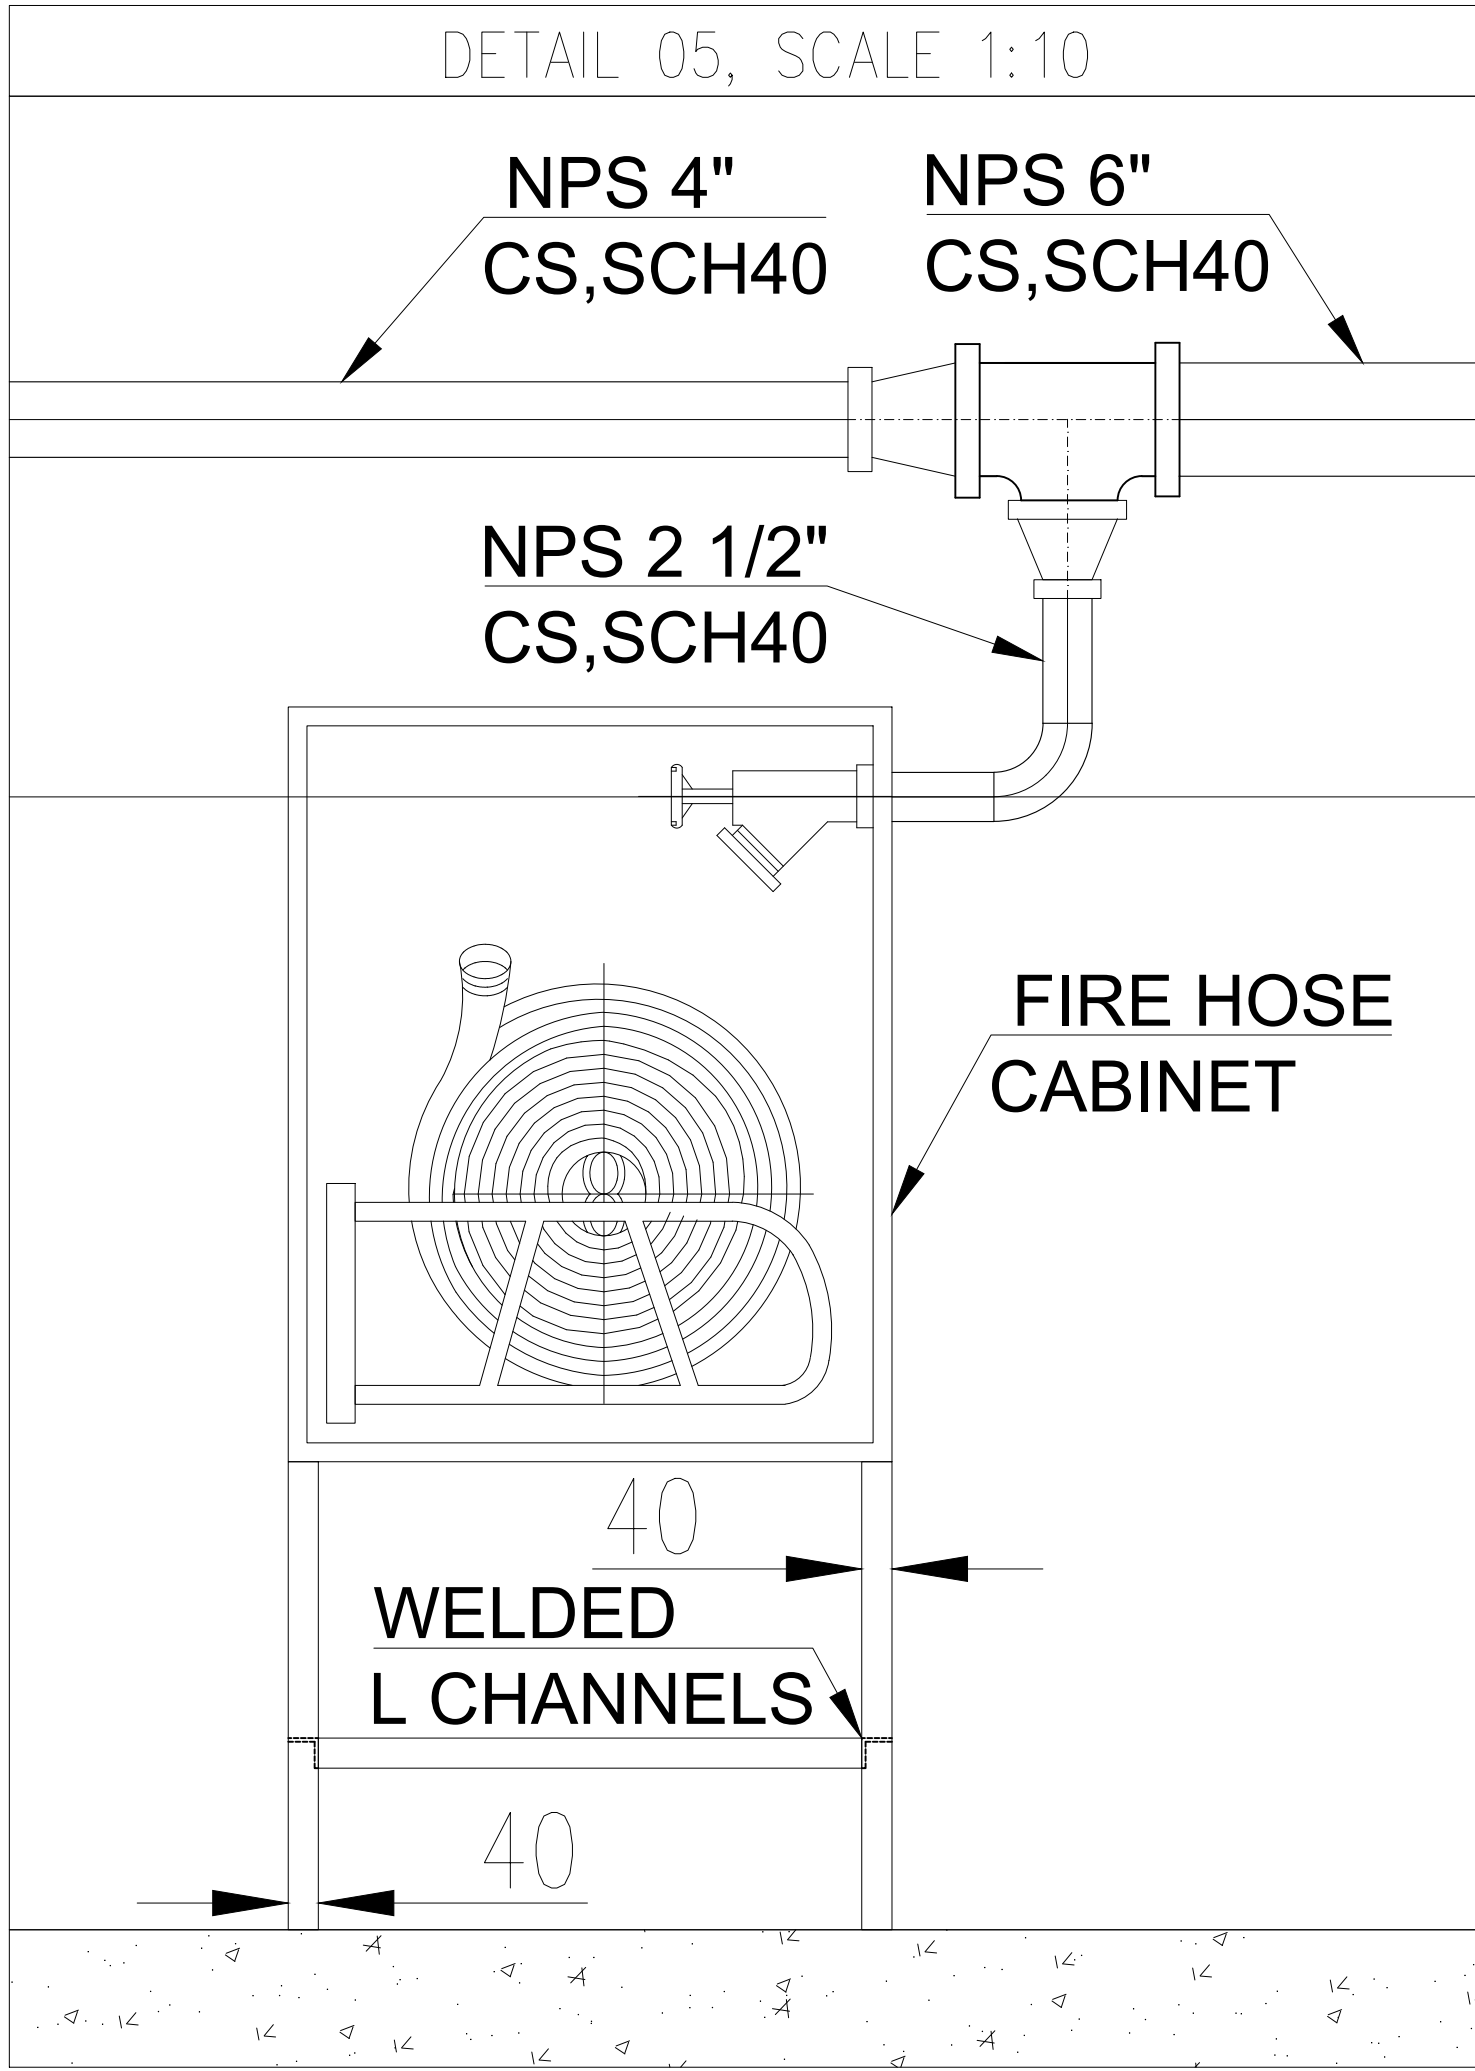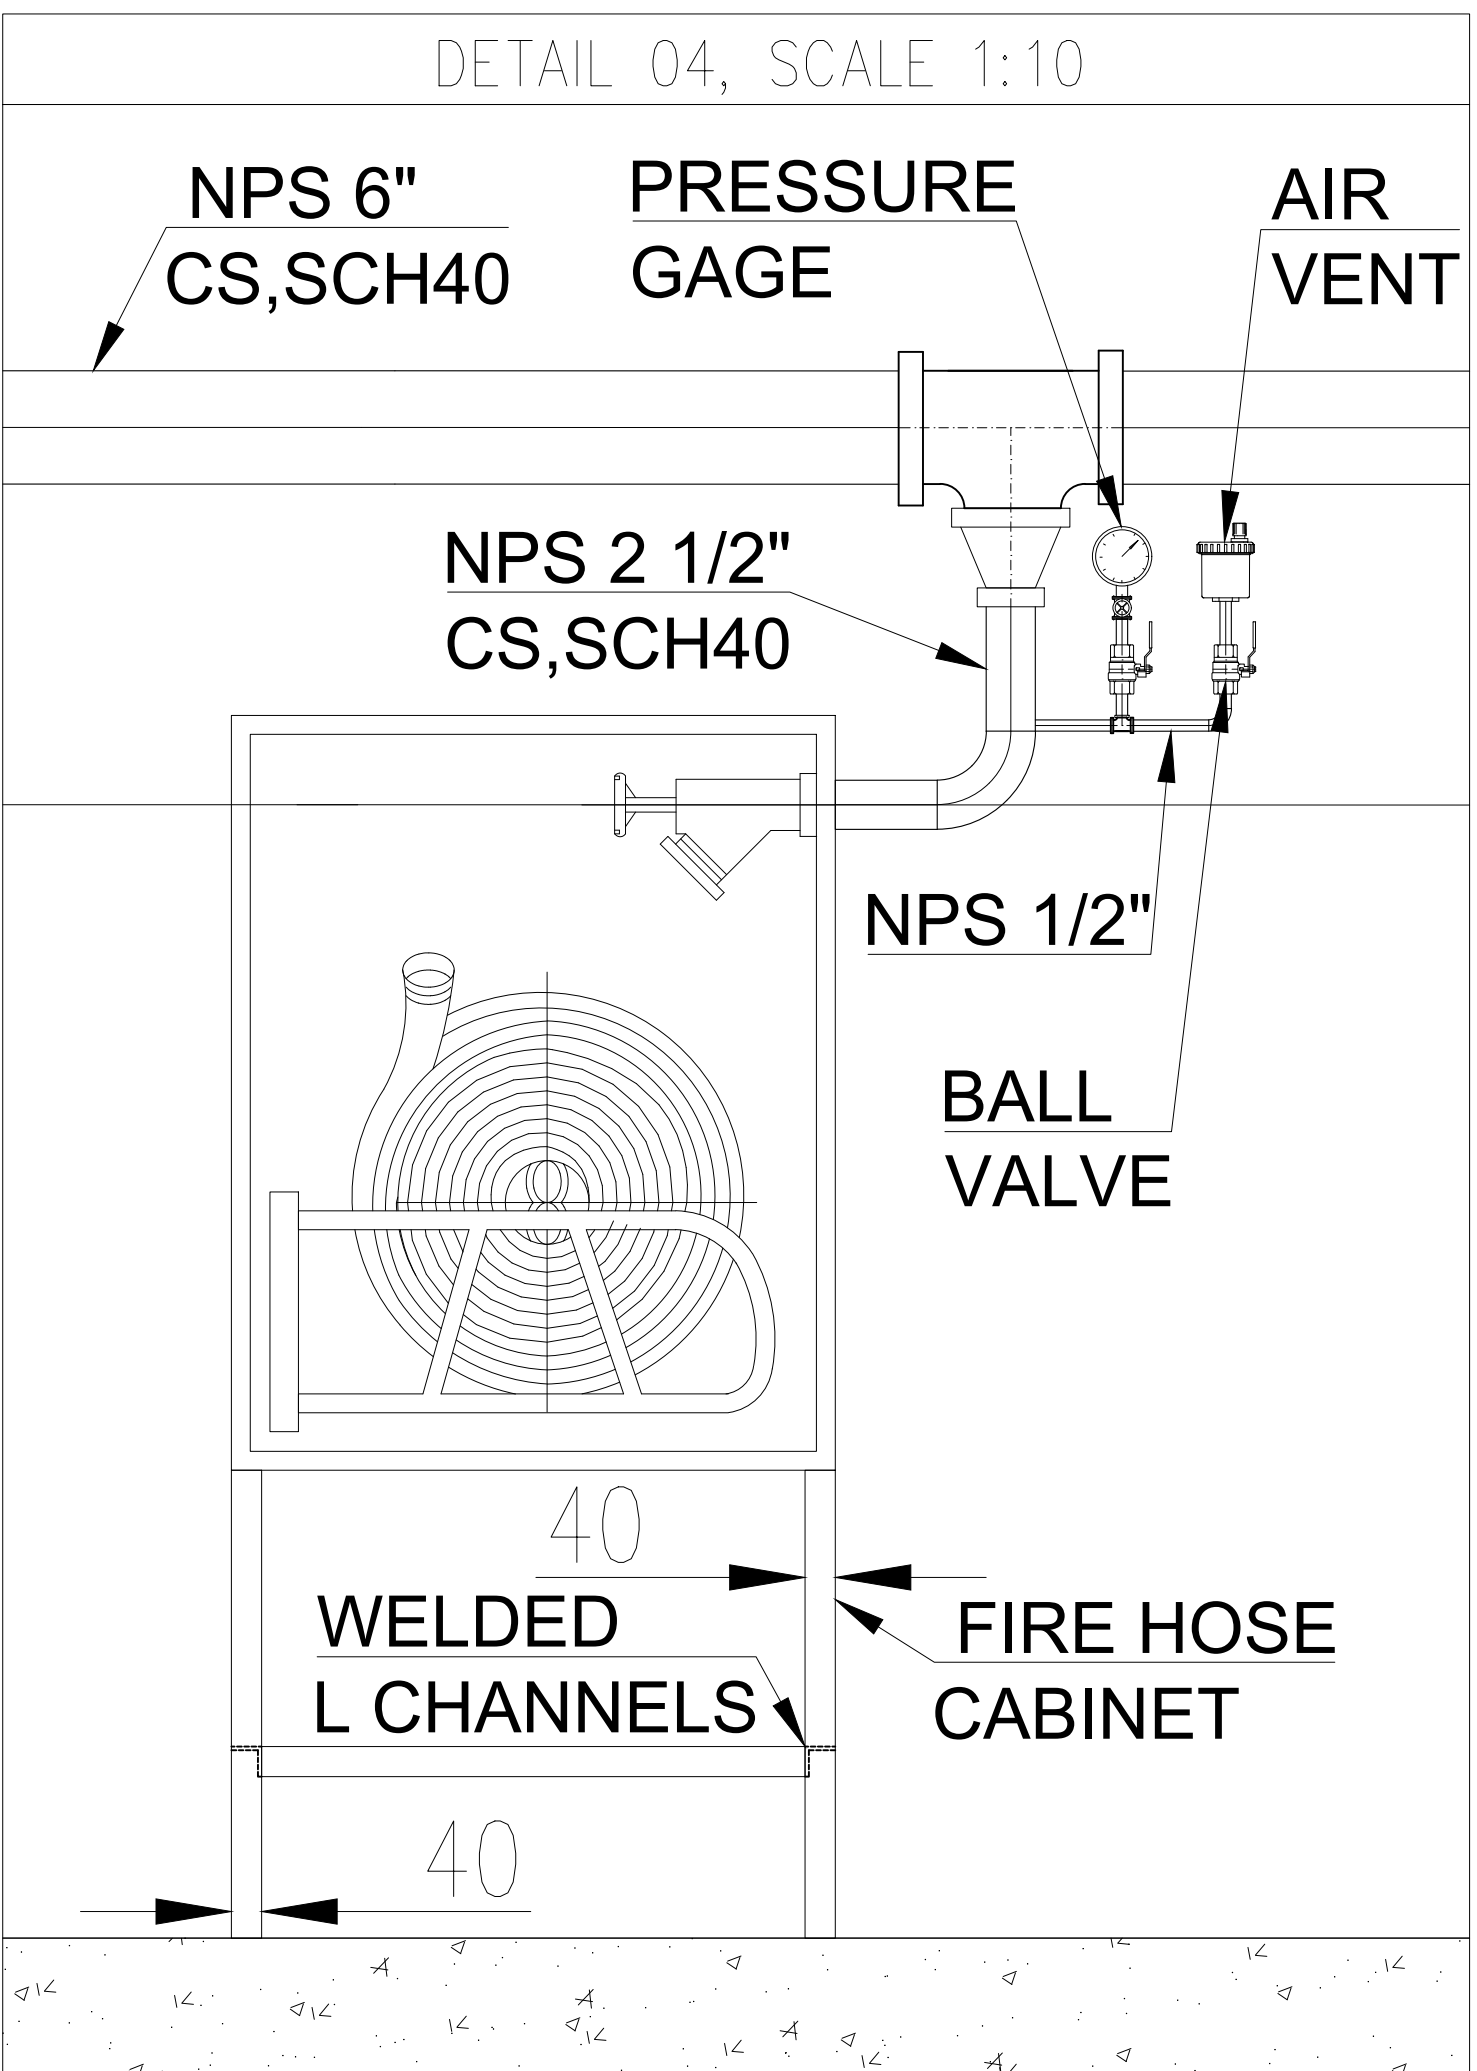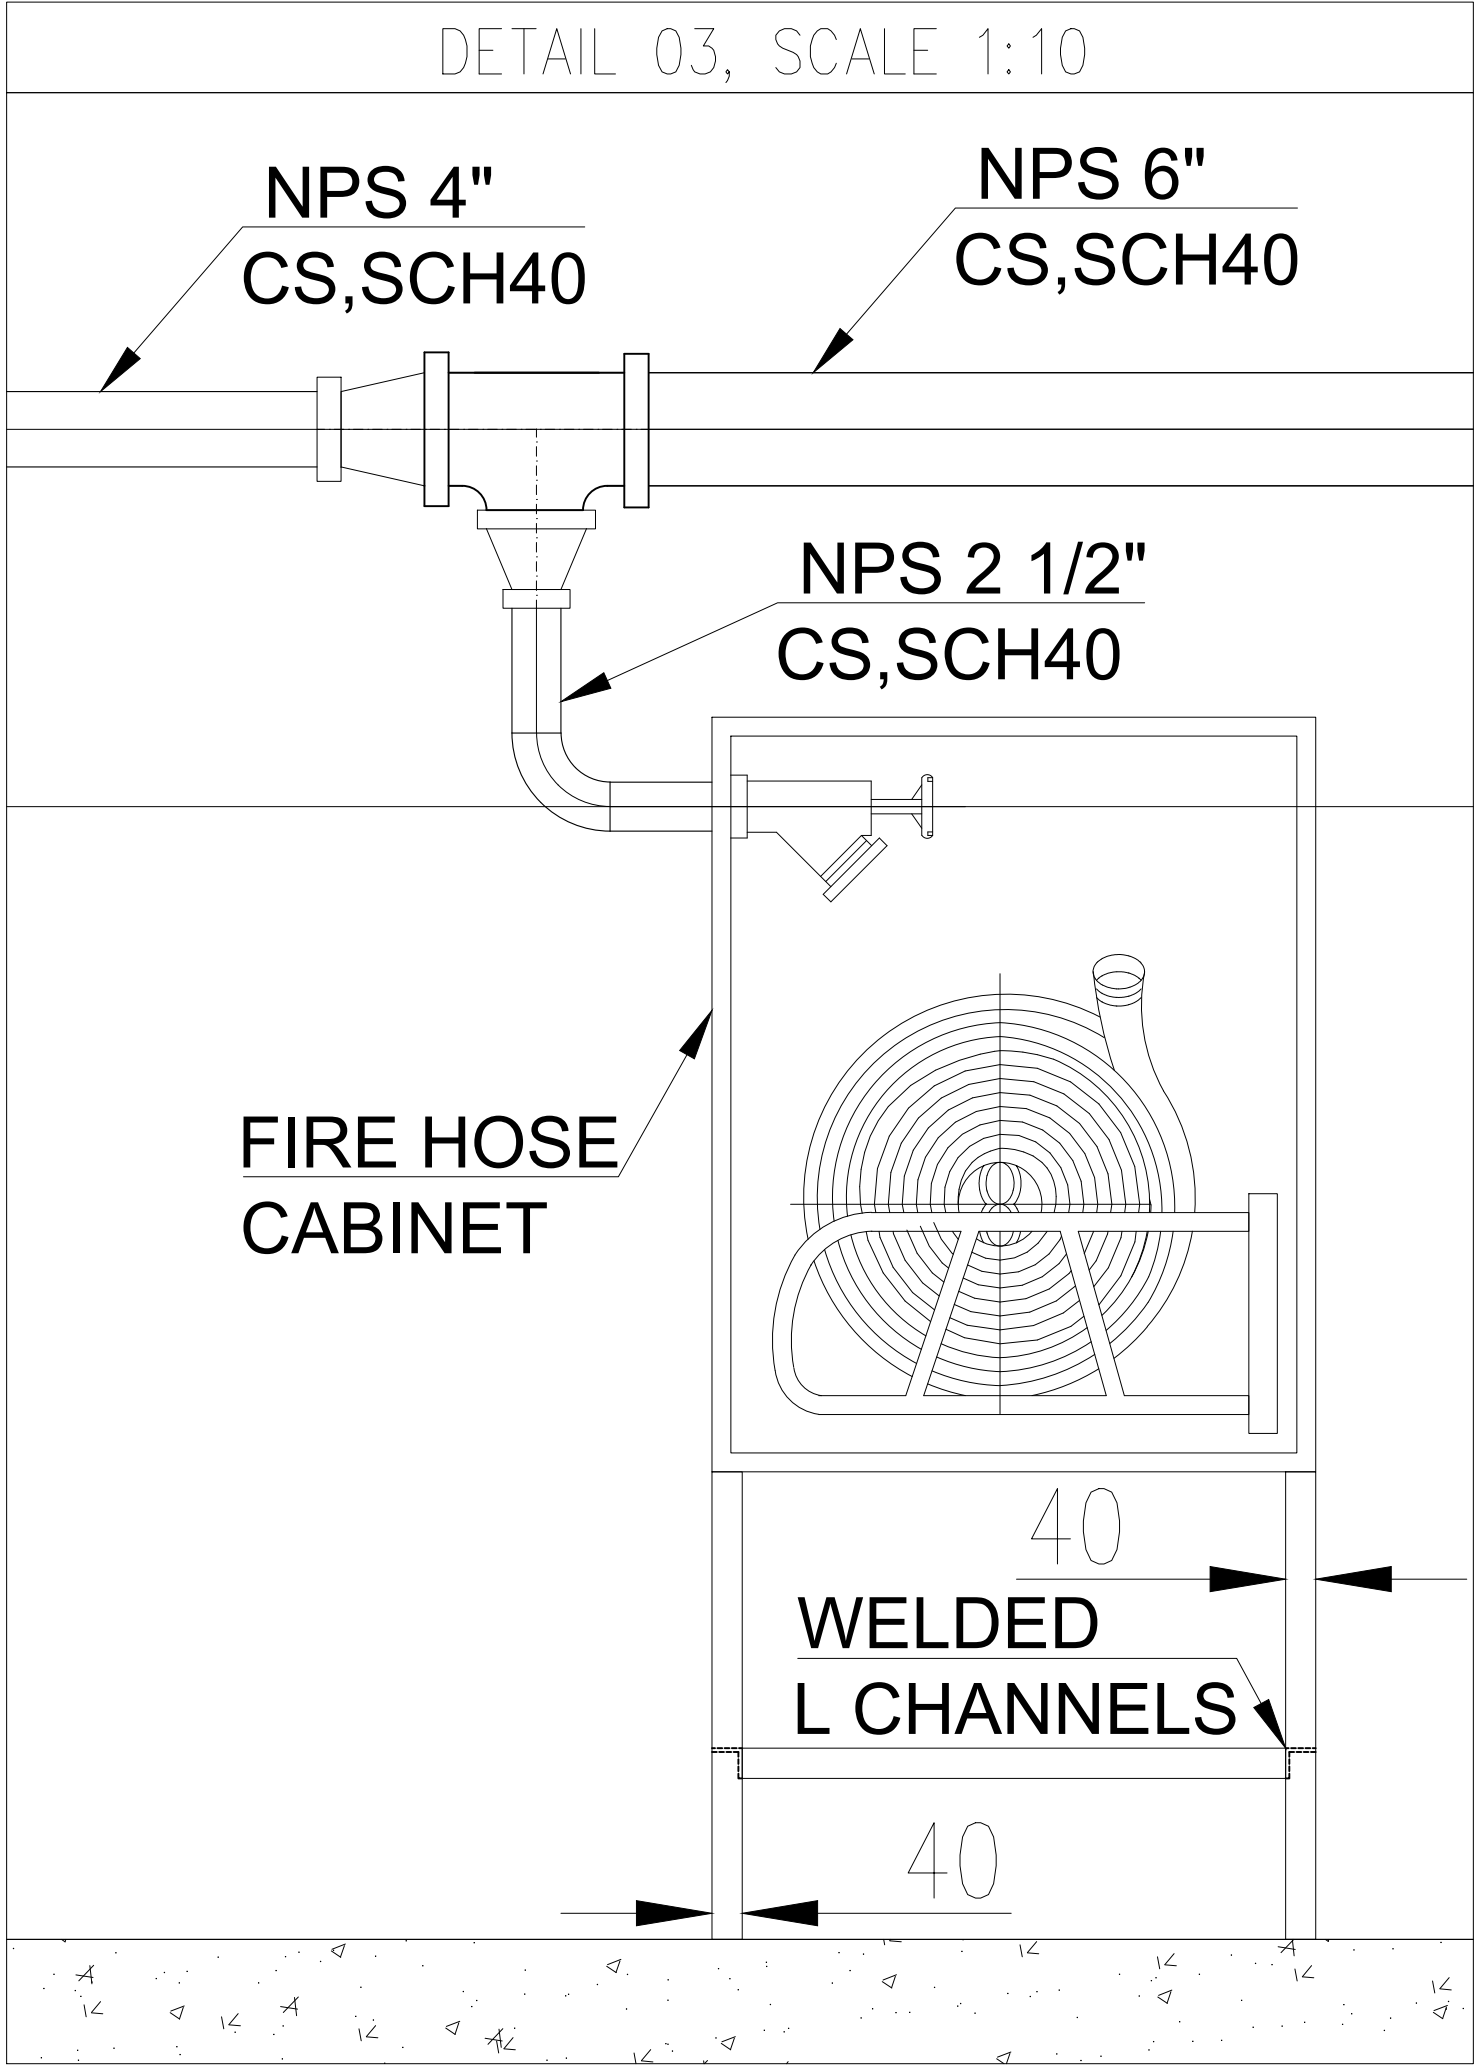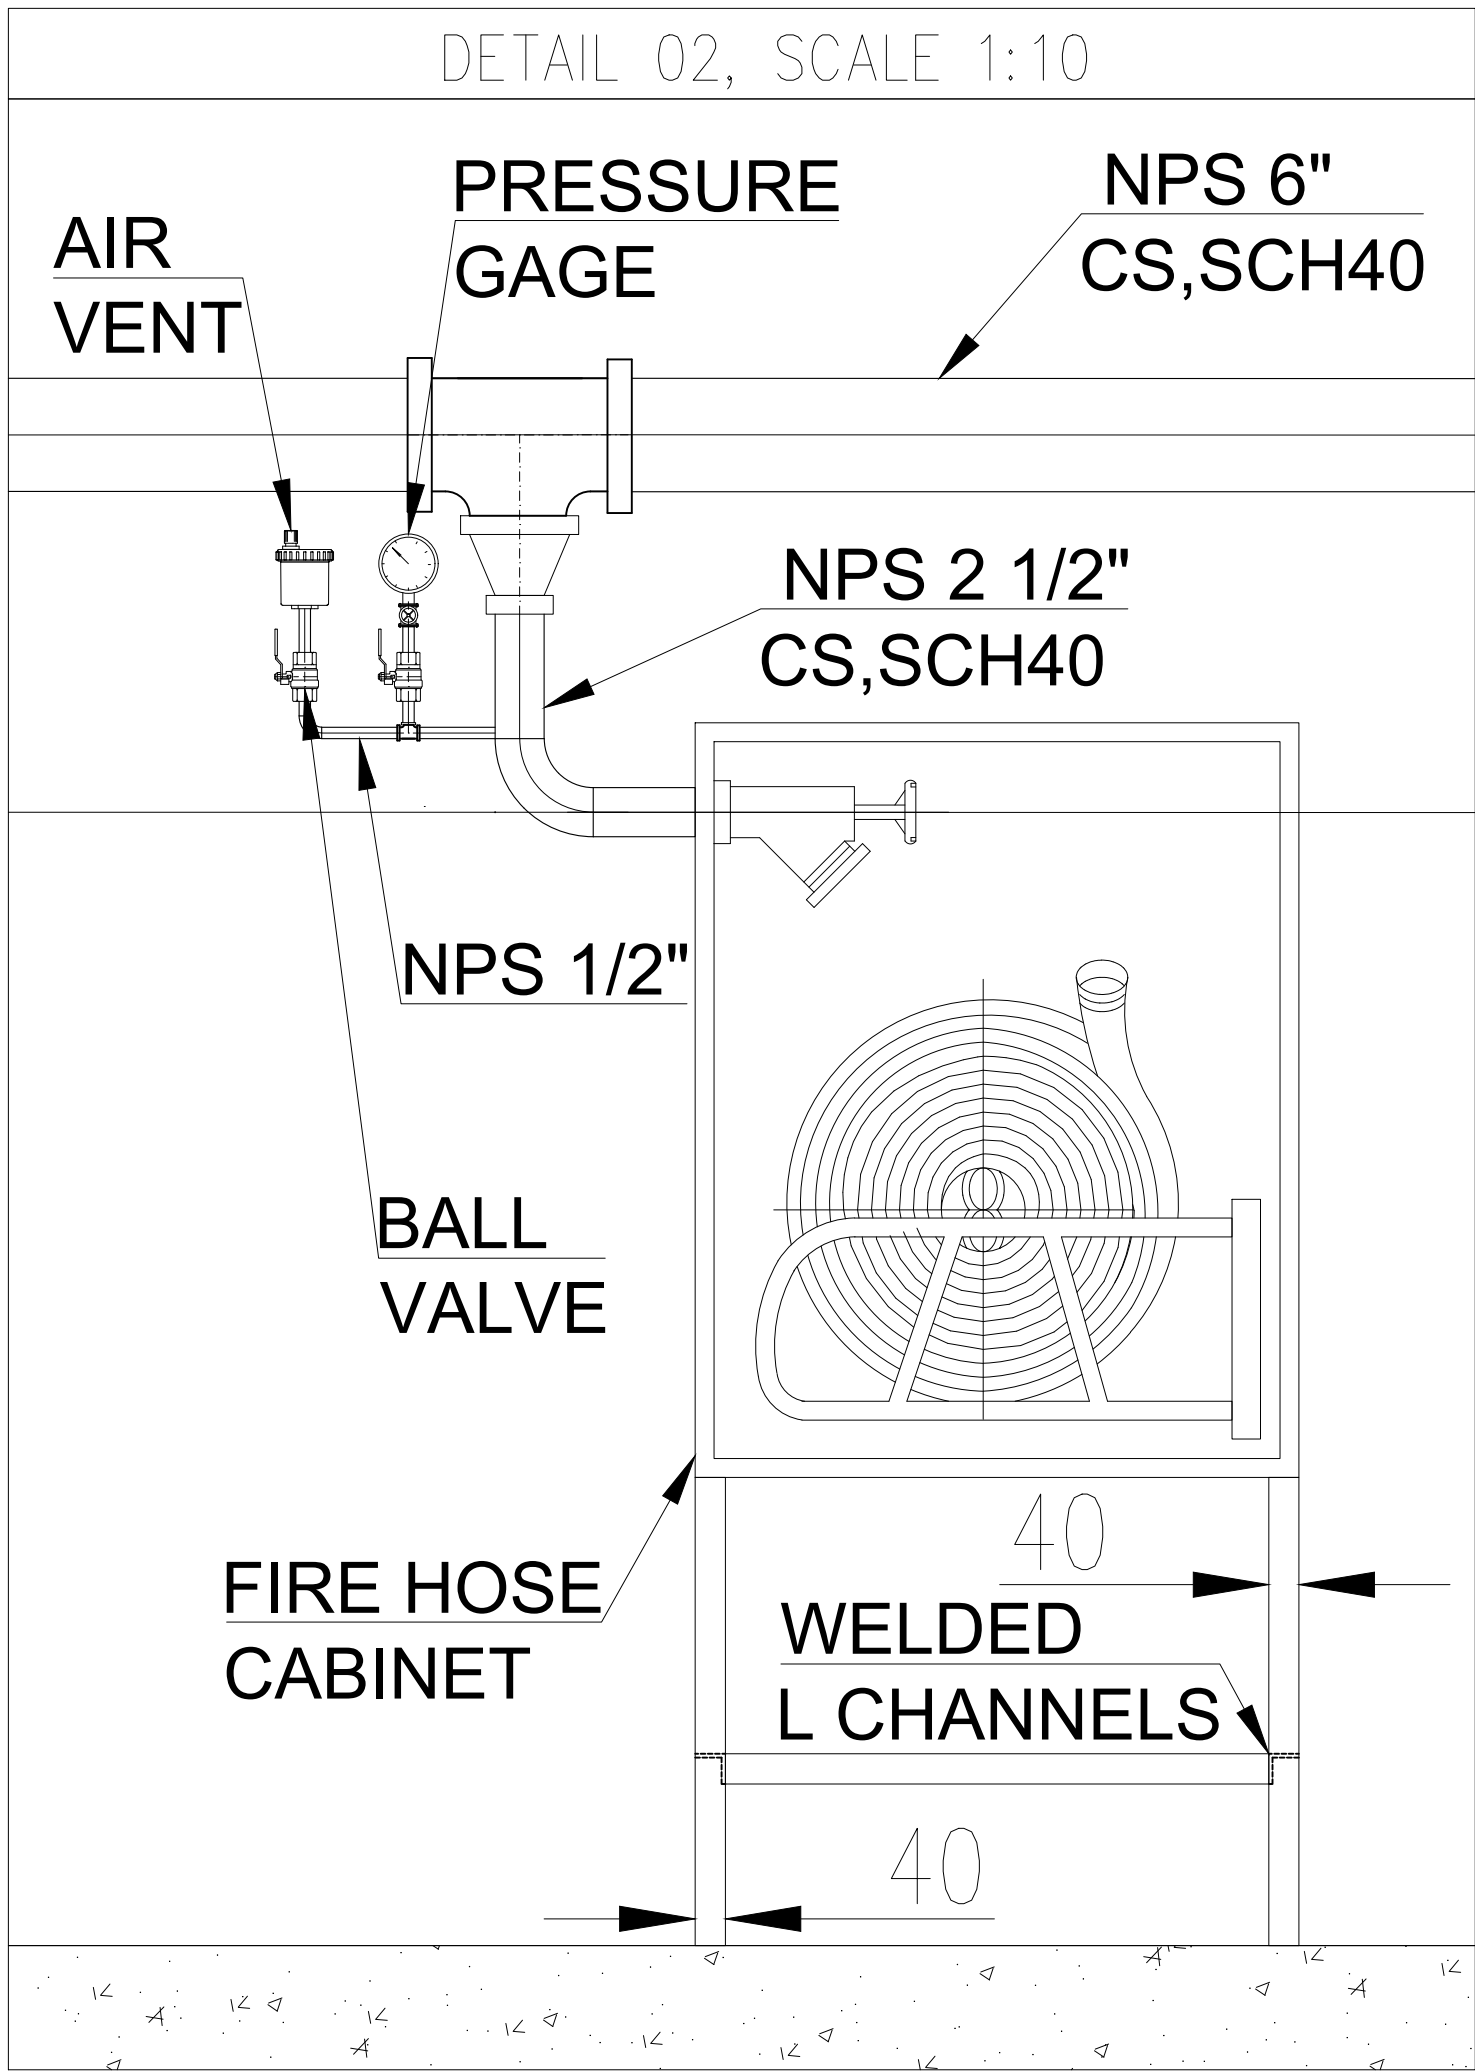

REFERENCE DRAWINGS	
GENERAL EXTERNAL LAYOUT AND ROAD SECTIONS	30A100DADD11030
DATASHEETS FOR FIREFIGHTING FIRE EXTINGUISHERS, CABINETS FOR HOSE REEL, FIRE HOSE REEL, REEL HOSE AND FIRE HYDRANTS	30A100DPGA05010
FIRE FIGHTING CALCULATION NOTE	30A100DPCA16020
FIXED FIRE-FIGHTING SYSTEMS P&I DIAGRAMS	30A100DPFM16030
ELECTRICAL ROOM - FIRE FIGHTING LAYOUT	30A100DPDD16100
SERVICES BUILDING - FIRE FIGHTING LAYOUT	30A100DPDD16070
SITE WATER SUPPLY CALCULATION NOTE	30A100DPEW14020

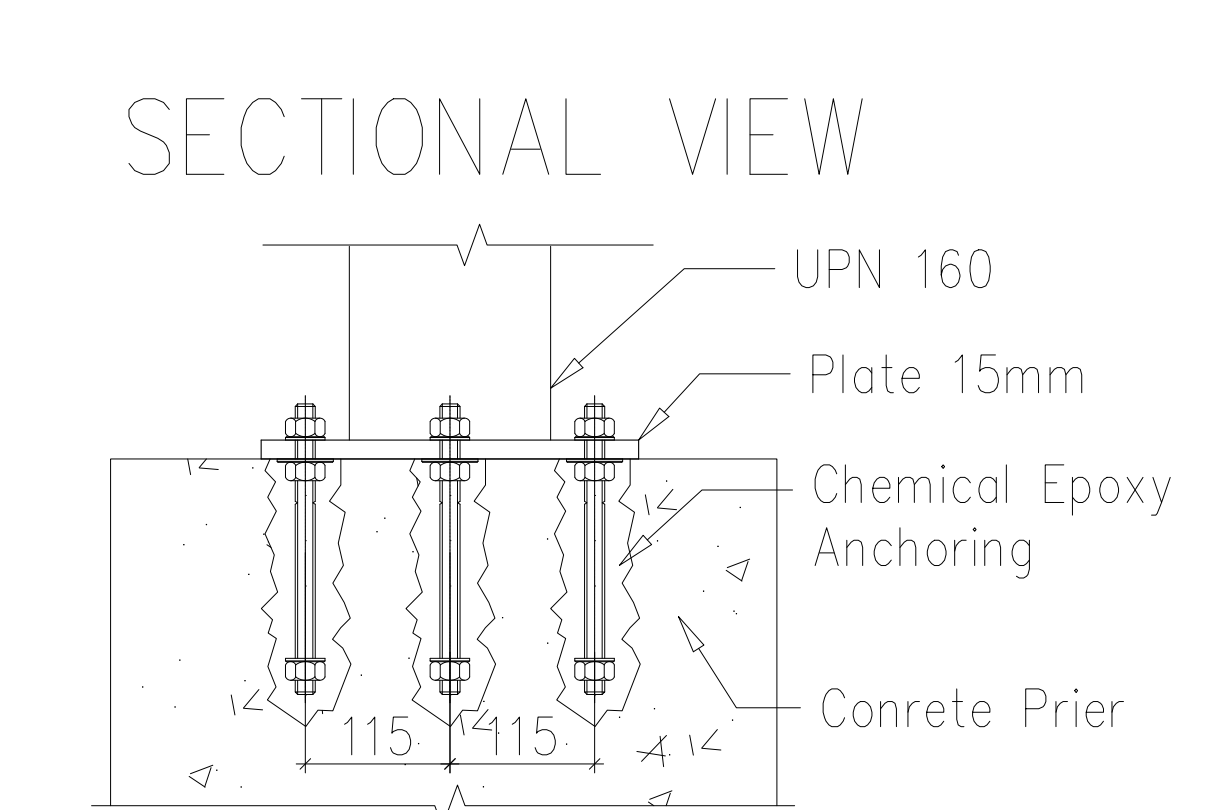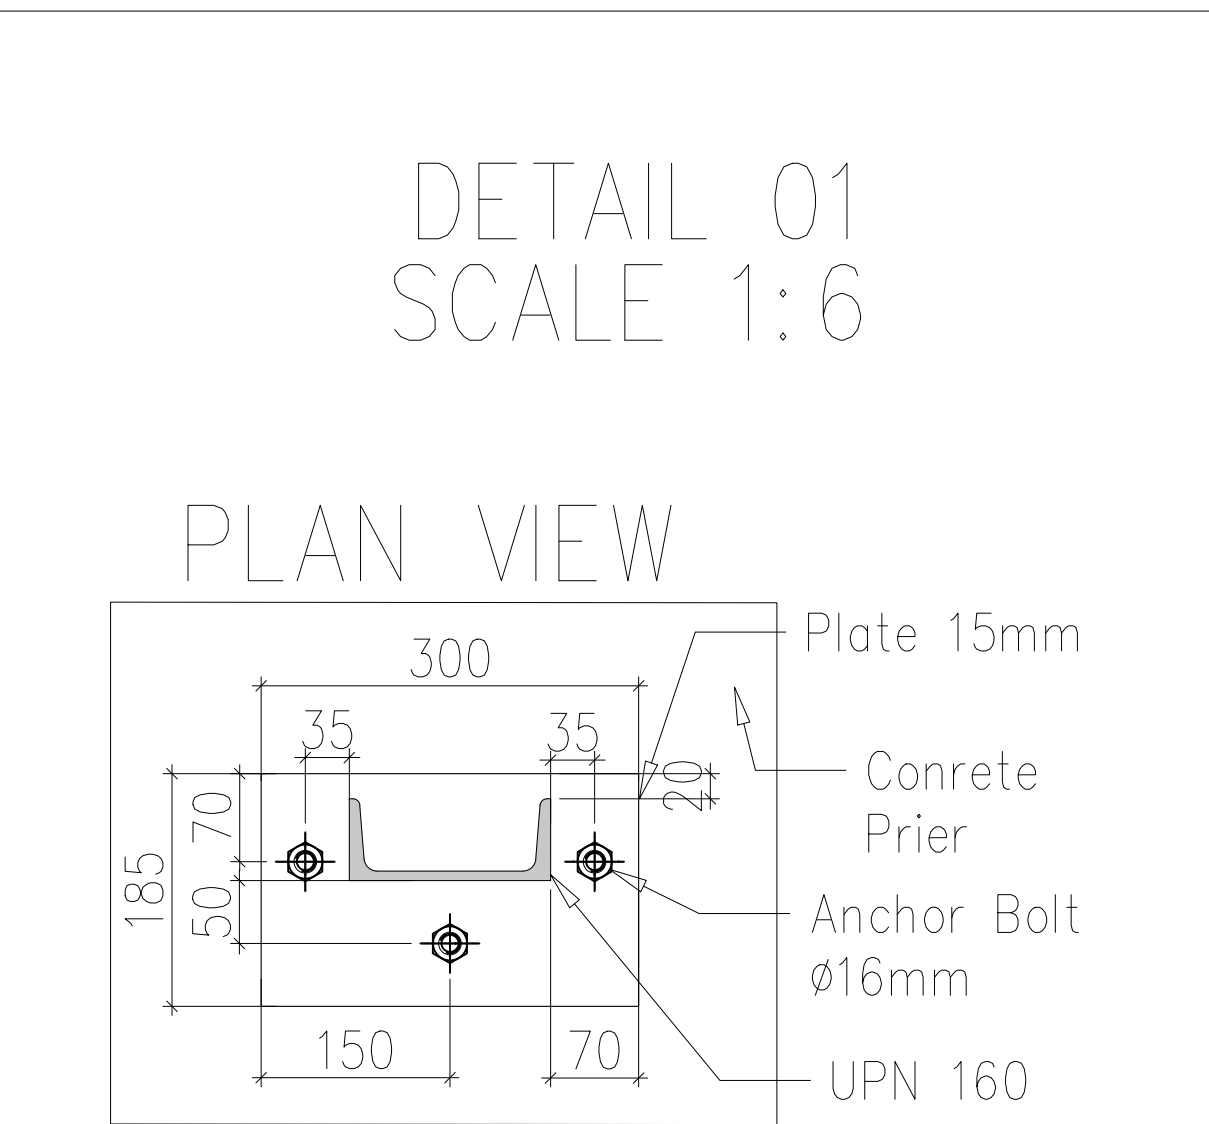

EX-DE	09	22/08/2024	Issue for Approval	R. SAAD	RO. HABIB	R. JALBOUT	M. PATURZO
EX-DE	08	23/07/2024	Issue for Approval	R. SAAD	RO. HABIB	R. JALBOUT	M. PATURZO
EX-DE	07	23/07/2024	Issue for Approval	R. SAAD	RO. HABIB	R. JALBOUT	M. PATURZO
EX-DE	06	23/05/2024	Issue for Approval	R. SAAD	RO. HABIB	R. JALBOUT	M. PATURZO
EX-DE	05	21/03/2024	Issue for Approval	R. SAAD	RO. HABIB	R. JALBOUT	N. CAPRETTI
EX-DE	04	06/12/2023	Issue for Approval	R. SAAD	RO. HABIB	R. JALBOUT	N. CAPRETTI
EX-DE	03	14/08/2023	Issue for FINAL	R. SAAD	RO. HABIB	R. JALBOUT	N. CAPRETTI
EX-DE	02	06/08/2023	Issue for Approval	R. SAAD	RO. HABIB	R. JALBOUT	N. CAPRETTI
EX-DE	01	28/02/2023	Issue for Approval	R. SAAD	RO. HABIB	R. JALBOUT	N. CAPRETTI
EX-DE	00	16/02/2023	Issue for Comments	R. SAAD	RO. HABIB	R. JALBOUT	N. CAPRETTI
Validity Status	Revision number	Date	Description	Contractor Prepared	Contractor Checked	Contractor Approved	Company Approved
Company Logo and Business Name				Project Name		Company Document ID:	
Eni Congo S.A.				CONGO BIOFUEL		30A100DPDD14040	
Contractor Logo and Business Name				Contract N.		Contractor Document ID:	
ZEROCK				Zerox Construction Congo S.a.r.l		30A100DPDD14040	
Facility and Sub Facility Name				Sheet Size:		Job N.	
1st Agri Hub - Industrial Start-Up - General				A1		Scale	
						NTS	
						Sheet of Sheets	
						8/8	
Document Title				Superseded by N.			
SITE WATER SUPPLY AND FIRE FIGHTING SYSTEM LAYOUT							
DETAILS				Plant Area		Plant Unit	
				NA		NA	